


1301호 · 가구 배치 버전 3

홀 8석 | 위쪽 소회의실 6석 | 아래쪽 메인 회의실 8석 | 보관 책상 9대

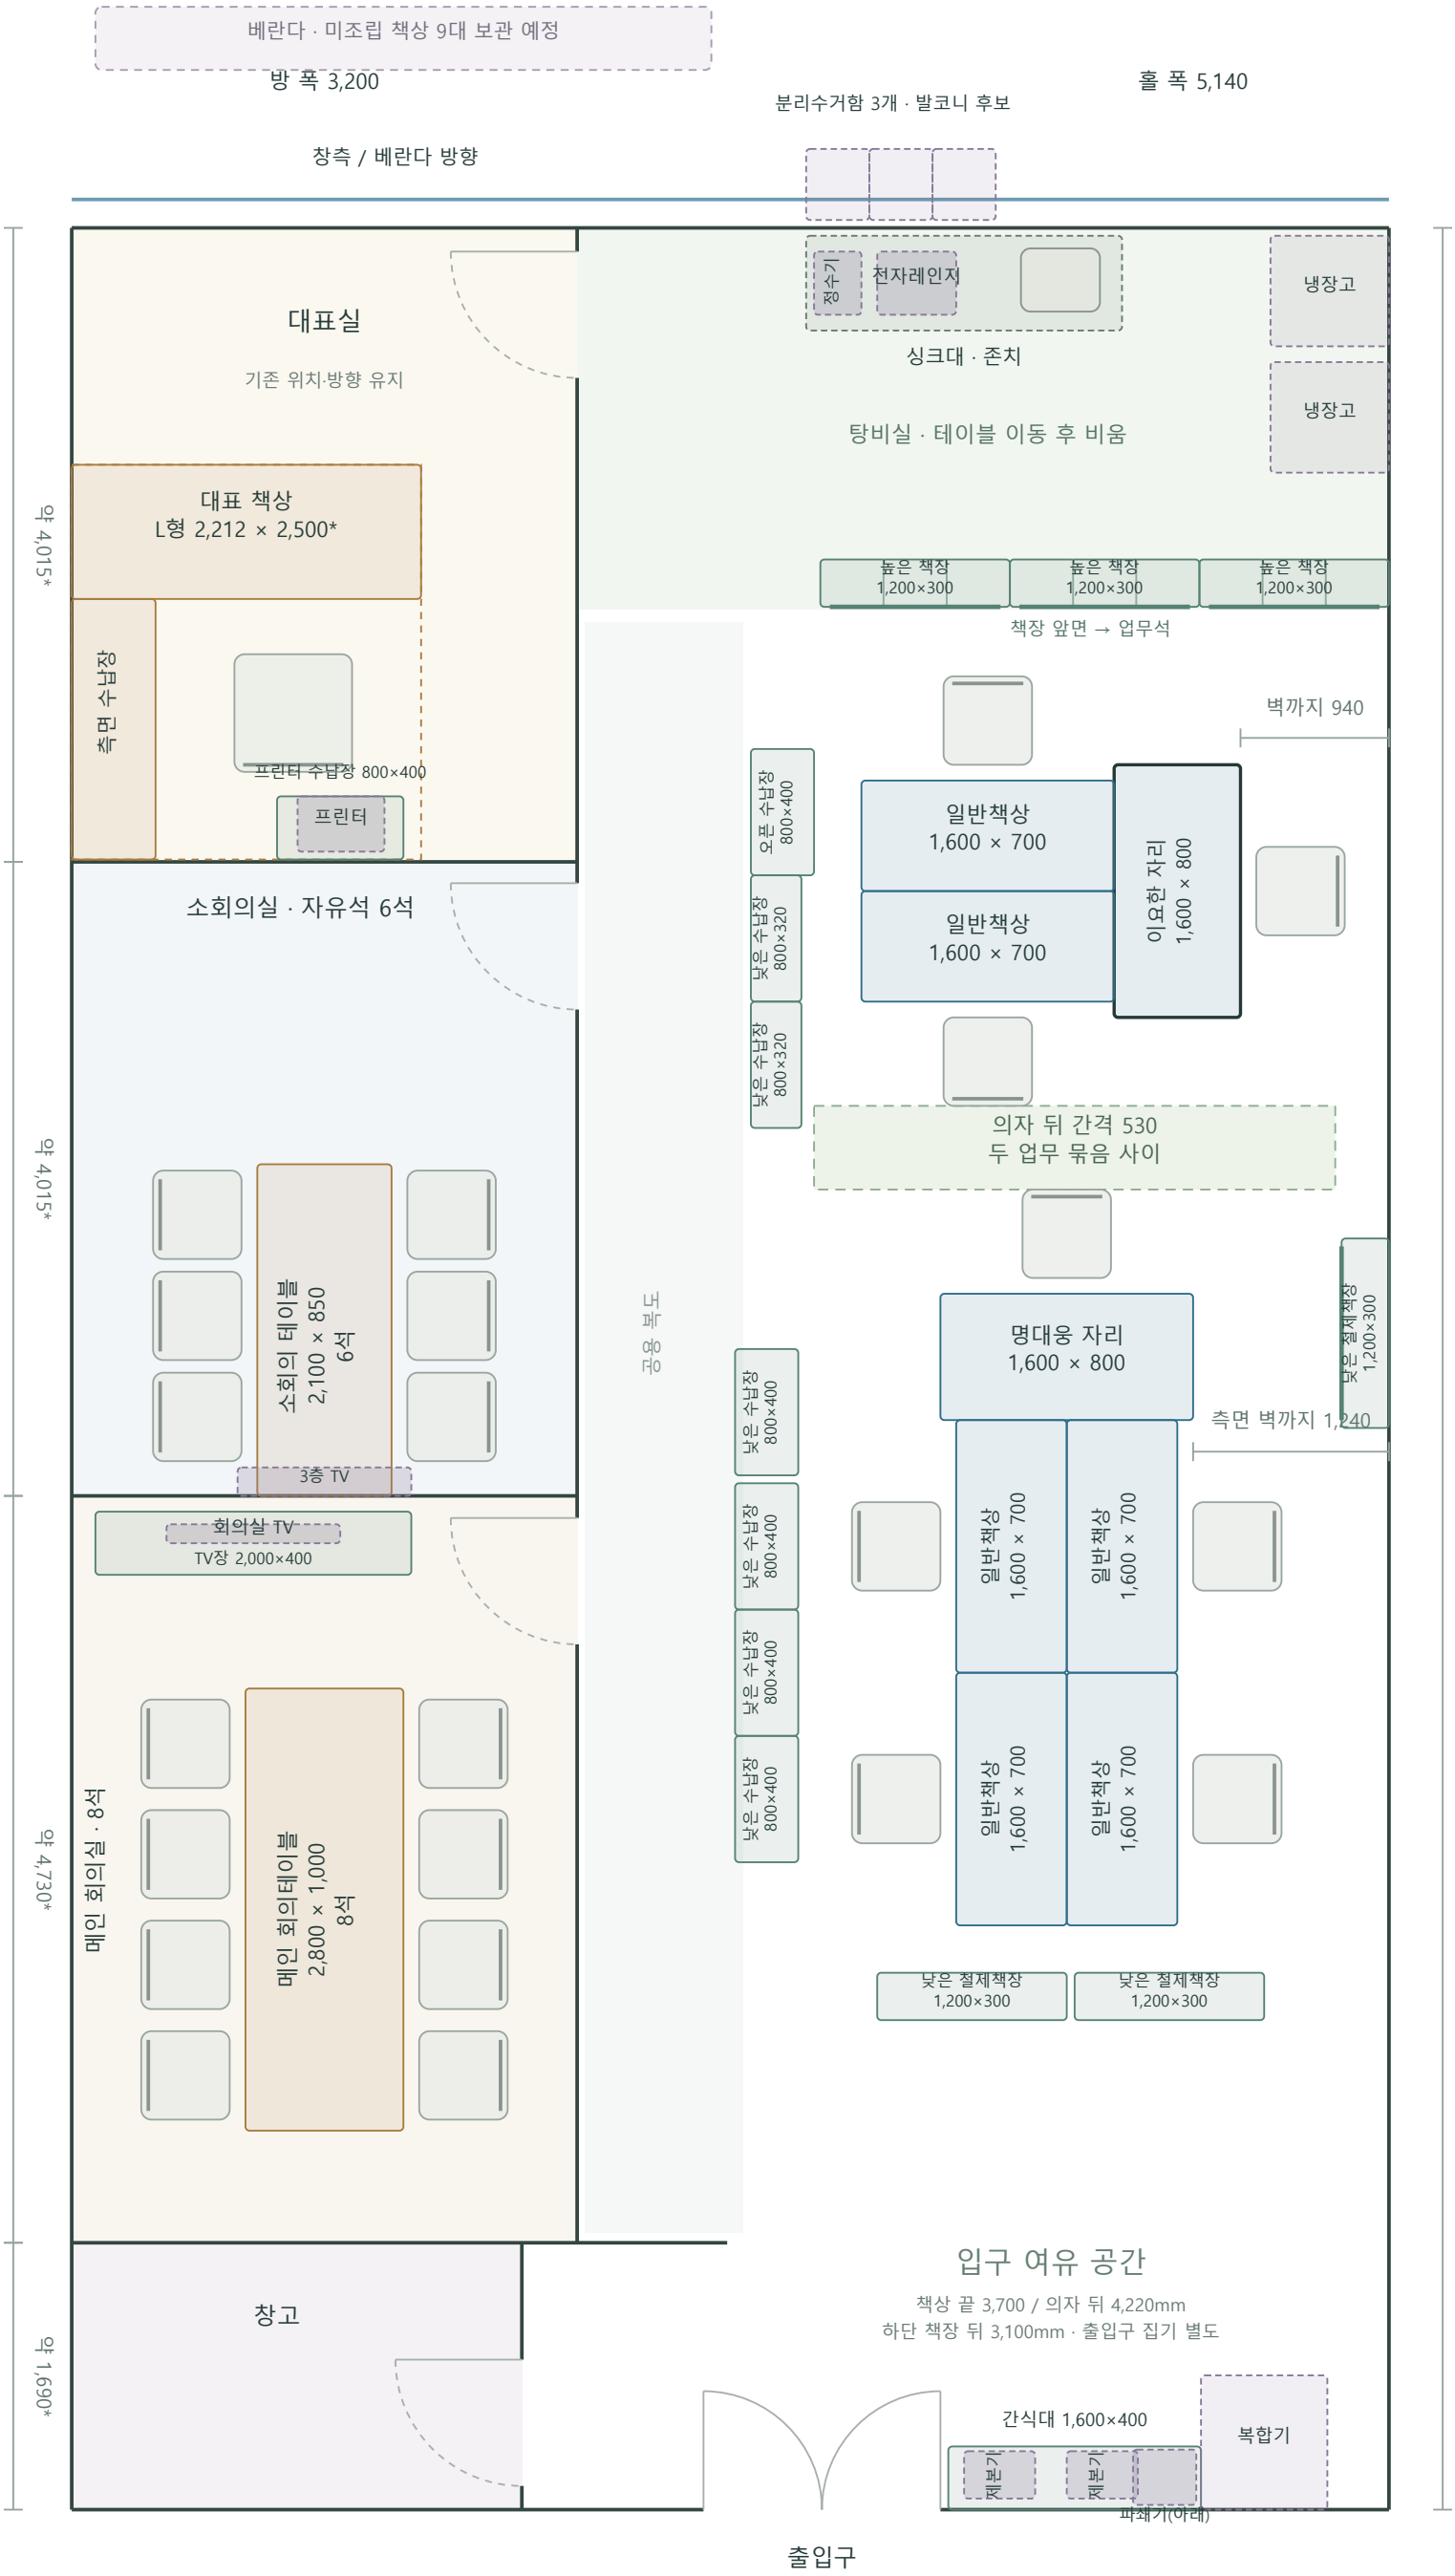

변경 사항 · 가구 목록 · 현장 확인

구역	버전 2	버전 3	변경 내용
홀 업무석	버전 2: 9석	버전 3: 8석	위 3석 + 아래 5석. 베이직데스크 1대 보관
명대웅 자리	오른쪽 벽 쪽 세로	4석 묶음 위쪽 가로	의자는 탕비실 쪽, 입구 방향을 바라봄
낮은 철제책장	오른쪽 벽 3대	벽 1대 + 하단 가로 2대	이미지의 위치와 방향 반영
입구 깊이	V2 책상 끝 2450mm	V3 책상 끝 3700mm	1250mm 증가. 하단 책장 뒤는 3100mm
통로 표기	900mm 두 곳	두 묶음 사이 530mm	의자 가정 포함. 2×2 중앙은 책상이 붙어 있음
보관	8대	9대	1600×700 8대 + 베이직데스크 1600×800 1대

가구·기기 보유 목록 (의자·부착 스크린 제외 / 단위 mm)

구분	품목	규격	보유	배치	보관	위치·비고
업무 책상	모션데스크 프리미엄	1600×800	2	2	0	홀: 이요한 / 명대웅
업무 책상	컴퓨터데스크	1600×700	4	3	1	홀에 3대 / 1대 베란다 보관
업무 책상	스크린 일체 일반책상	1600×700	10	3	7	홀에 3대 / 7대 베란다 보관
업무 책상	베이직데스크	1600×800	1	0	1	베란다 미조립 보관
대표실	대표 L형 모션데스크	2212×2500*	1	1	0	대표실, 기존 방향 유지
회의	데스커 빅테이블	2800×1000	1	1	0	아래 메인 회의실 / 8석
회의	기존 3층 회의 테이블	2100×850	1	1	0	위 소회의실 / 아래쪽 벽 밀착 / 6석
수납	높은 책장·선반	1200×300	3	3	0	탕비 경계, 앞면은 업무석 방향
수납	낮은 철제책장 3단	1200×300	3	3	0	오른쪽 벽 1 / 하단 가로 2
수납	낮은 수납장	800×400	4	4	0	복도 경계, 같은 규격 4개 일렬
수납	낮은 수납장	800×320	2	2	0	복도 위쪽 경계
수납	상부 오픈·하부 도어 수납장	800×400	1	1	0	복도 위쪽 경계
수납	대표실 프린터 수납장	800×400	1	1	0	대표실 Canon 프린터 아래
수납	간식대	1600×400	1	1	0	입구 오른쪽
수납	TV장	2000×400	1	1	0	메인 회의실 문 쪽
기기	TV	외곽 가정*	2	2	0	메인 회의실 TV장 / 소회의실 테이블 위
기기	복합기 / Canon 프린터	외곽 가정*	각 1	각 1	0	입구 오른쪽 / 대표실
기기	제본기 / 파쇄기	외곽 가정*	2 / 1	2 / 1	0	간식대 위 2 / 아래 1
탕비	냉장고	외곽 가정*	2	2	0	탕비실 오른쪽
탕비	정수기 / 전자레인지	외곽 가정*	각 1	각 1	0	기존 싱크대 위
탕비	싱크대(존치)	약 2000×600*	1	1	0	현재 위치 유지
탕비	분리수거함	외곽 가정*	3	3	0	발코니 후보, 위치 확인

검토 사항

1. 사용자 이미지 기준 버전 3. 홀 8석(이요한 쪽 3석 + 명대웅 쪽 5석), 대표실 1석 별도. 이요한 쪽 3석은 높은 책장에서 멀어지도록 V2보다 입구 쪽으로 300mm 이동. 좌표는 이미지 비례로 재구성하며 캡처에서 약 50mm 겹친 두 일반책상은 맞붙여 정리.
2. 업무 책상 보유 17대 = 홀 배치 8대 + 베란다 보관 9대. 보관은 1600×700 8대와 1600×800 베이직데스크 1대. 베란다 표시는 보관 예정 위치 설명이며 실제 적재 외곽은 아님.
3. 입구 깊이: 마지막 업무 책상 끝 기준 3700mm(V1 2500 / V2 2450). 가장 입구에 가까운 의자 뒤 기준 4220mm(V1 1840 / V2 1890). 하단 책장까지 함께 고려한 가구 뒤 기준은 3100mm. 간식대·복합기·출입문 점유는 별도.
4. 사용자 캡처의 3700mm는 현재 배치에서 책상 끝 기준이며 의자 뒤 기준이 아님. 두 기준을 구분해 표시. 문 열림 깊이 750mm를 제외한 참고 깊이는 가구 뒤 기준 2350mm이며 전체 통로 폭을 뜻하지 않음.
5. 두 업무 묶음 사이: 책상 몸체 간 1850mm, 의자 560mm와 책상 간격 100mm를 양쪽 적용하면 530mm. 기존 900mm 통로 표시는 삭제하고 실제 계산값으로 정정. 명대웅 쪽 2×2 책상 중앙에는 횡단 통로 없음.
6. 이요한 책상 오른쪽 끝~벽 940mm, 의자 뒤~벽 약 280mm. 명대웅 책상 오른쪽 끝~벽 1240mm는 측면 간격이며 의자 뒤 여유가 아님. 옆 철제책장 깊이 300mm 제외 시 책상 옆 폭은 940mm.
7. 소회의실은 세로 2100×850 테이블 및 상판 TV를 아래쪽 벽에 밀착, 6석. 메인 회의실은 2800×1000 테이블, 긴 면 4+4 총 8석. 의자는 배치 기호이며 반입 수량과는 별도.
8. 전체 14.45×8.34m 가정 유지. 방 깊이·문·기동 돌출·기기 외곽은 실측 확인. 온라인에서 이동·회전 후 JSON 저장 가능. 다른 기기나 다른 사람에게 편집 내용이 자동 동기화되지는 않음.